


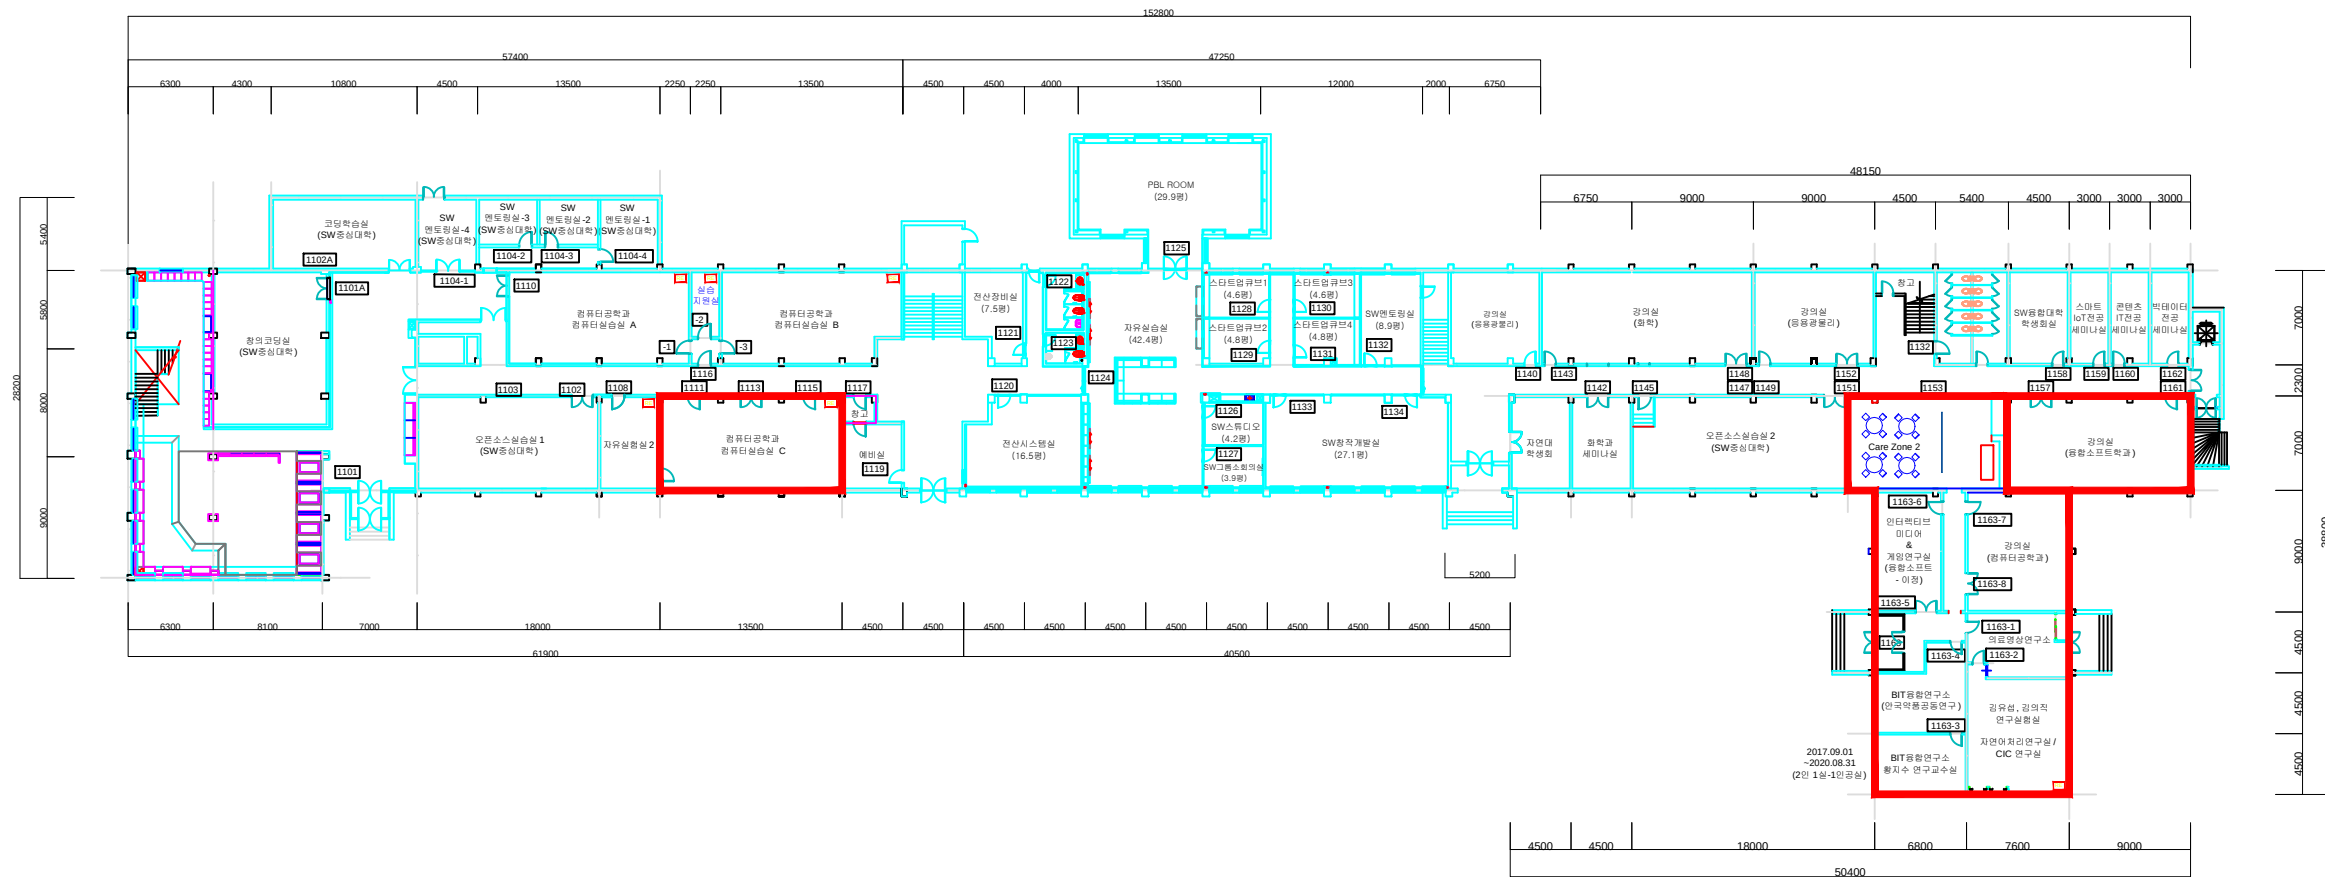

1층 평면도

NO.	DATE	REV.	DESCRIPT	DR.	CHK.
-----	------	------	----------	-----	------

설계
CONSULTANTS

작성
DRAWN BY:

심사
CHECKED BY:

승인
APPROVED BY:

작성
DRAWN BY:

심사
CHECKED BY:

심사
CHECKED BY:

승인
APPROVED BY:

승인
APPROVED BY:

도면명
DRAWING TITLE


1. 공학관1층

축척
SCALE

날짜
DATE

도면번호
DRAWING NO.

일련번호
SHEET NO.

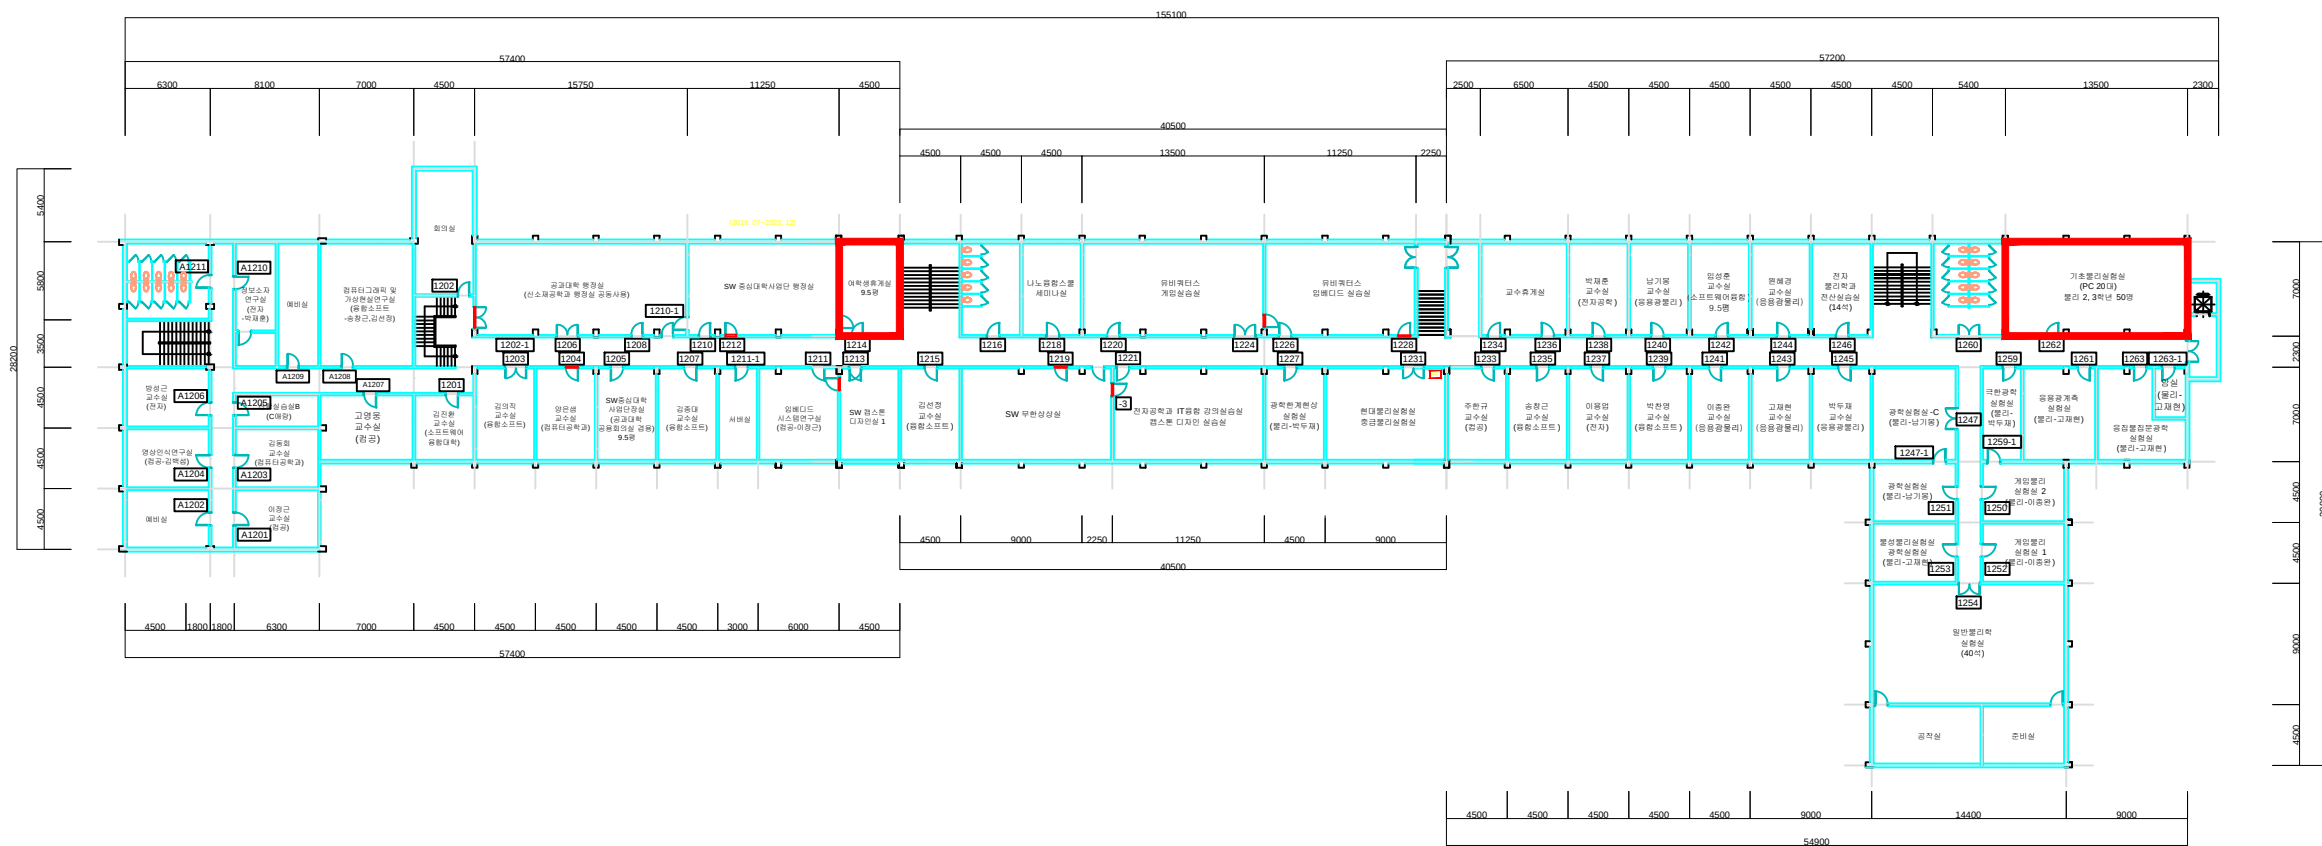

2층 평면도

NO. DATE REV. DESCRIPTION DPL. CHK.

CONSULTANTS

작성

DRAWN BY:

심사

CHECKED BY:

승인

APPROVED BY:

작성

DRAWN BY:

심사

CHECKED BY:

승인

APPROVED BY:

승인

APPROVED BY:

도면명

DRAWING TITLE

1. 공학관2층

축척

SCALE

날짜


DATE

도면번호

DRAWING NO.

일련번호

SHEET NO.

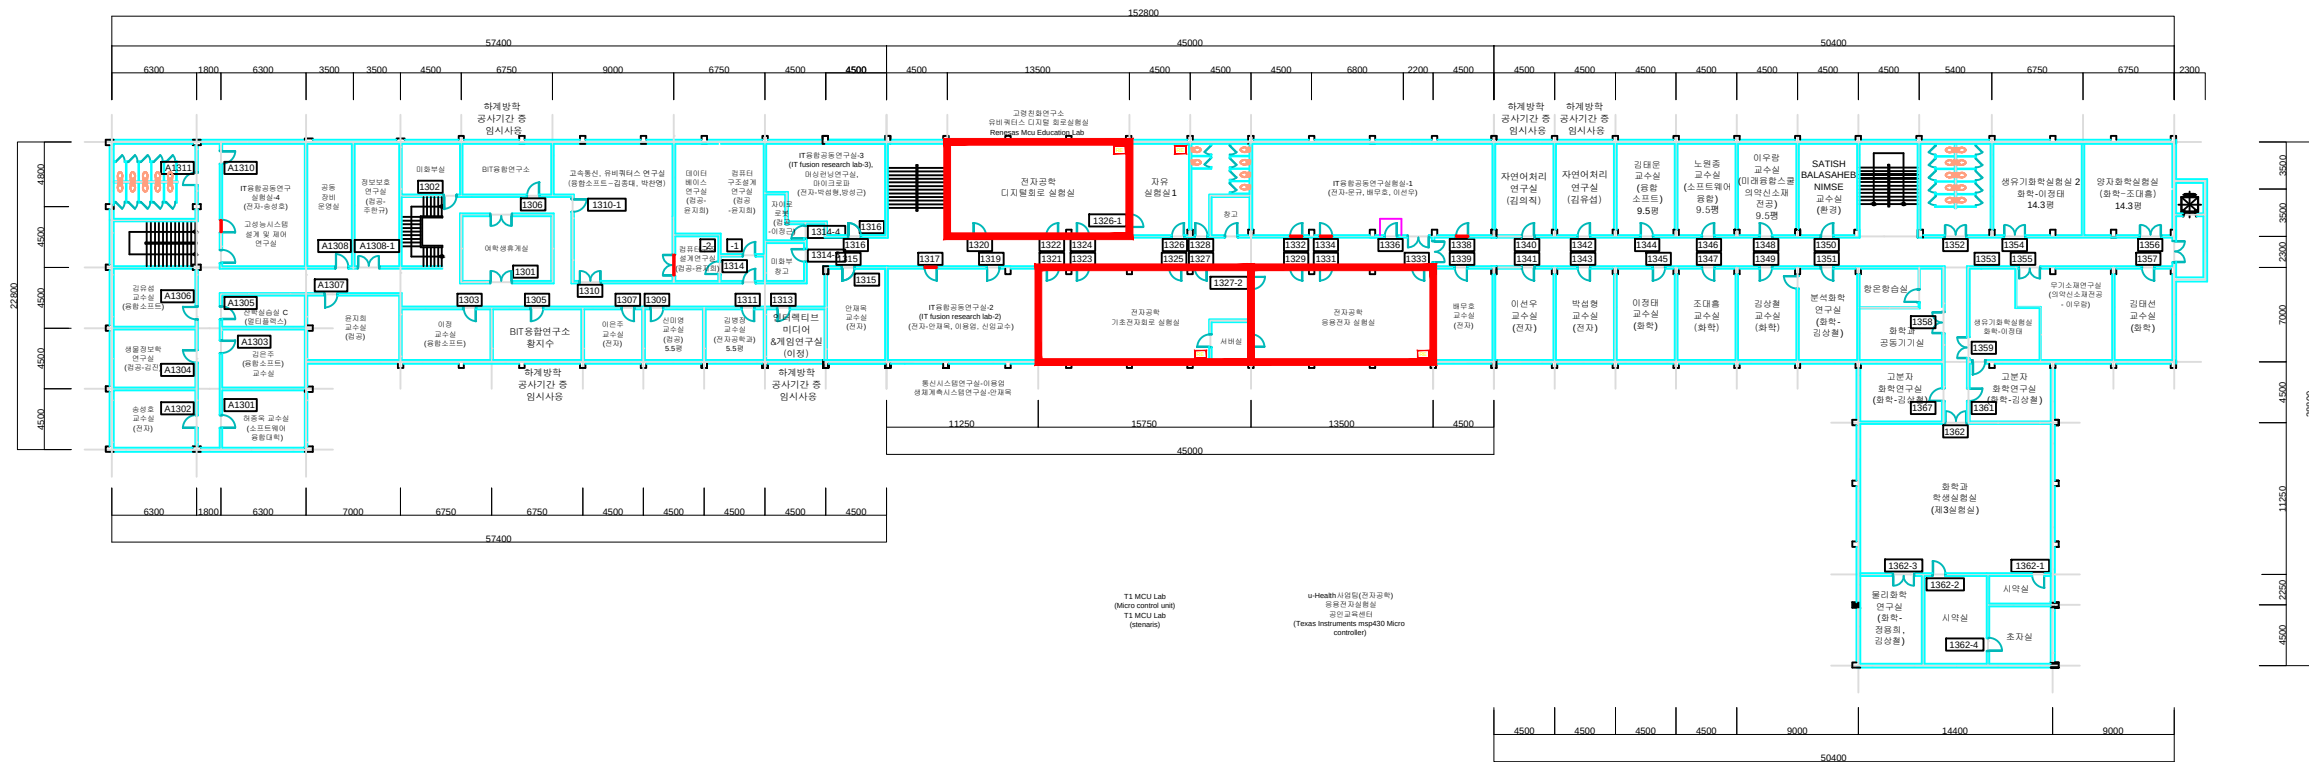

NO.	DATE	REV.	DESCRPT	DR.	CHK.
-----	------	------	---------	-----	------

설계
CONSULTANTS

작성
DRAWN BY:

심사
CHECKED BY:

승인
APPROVED BY:

작성
DRAWN BY:

심사
CHECKED BY:

심사
CHECKED BY:

승인
APPROVED BY:

승인
APPROVED BY:

도면명
DRAWING TITLE


1. 공학관3층

축척
SCALE

날짜
DATE

도면번호
DRAWING NO.

일련번호
SHEET NO.

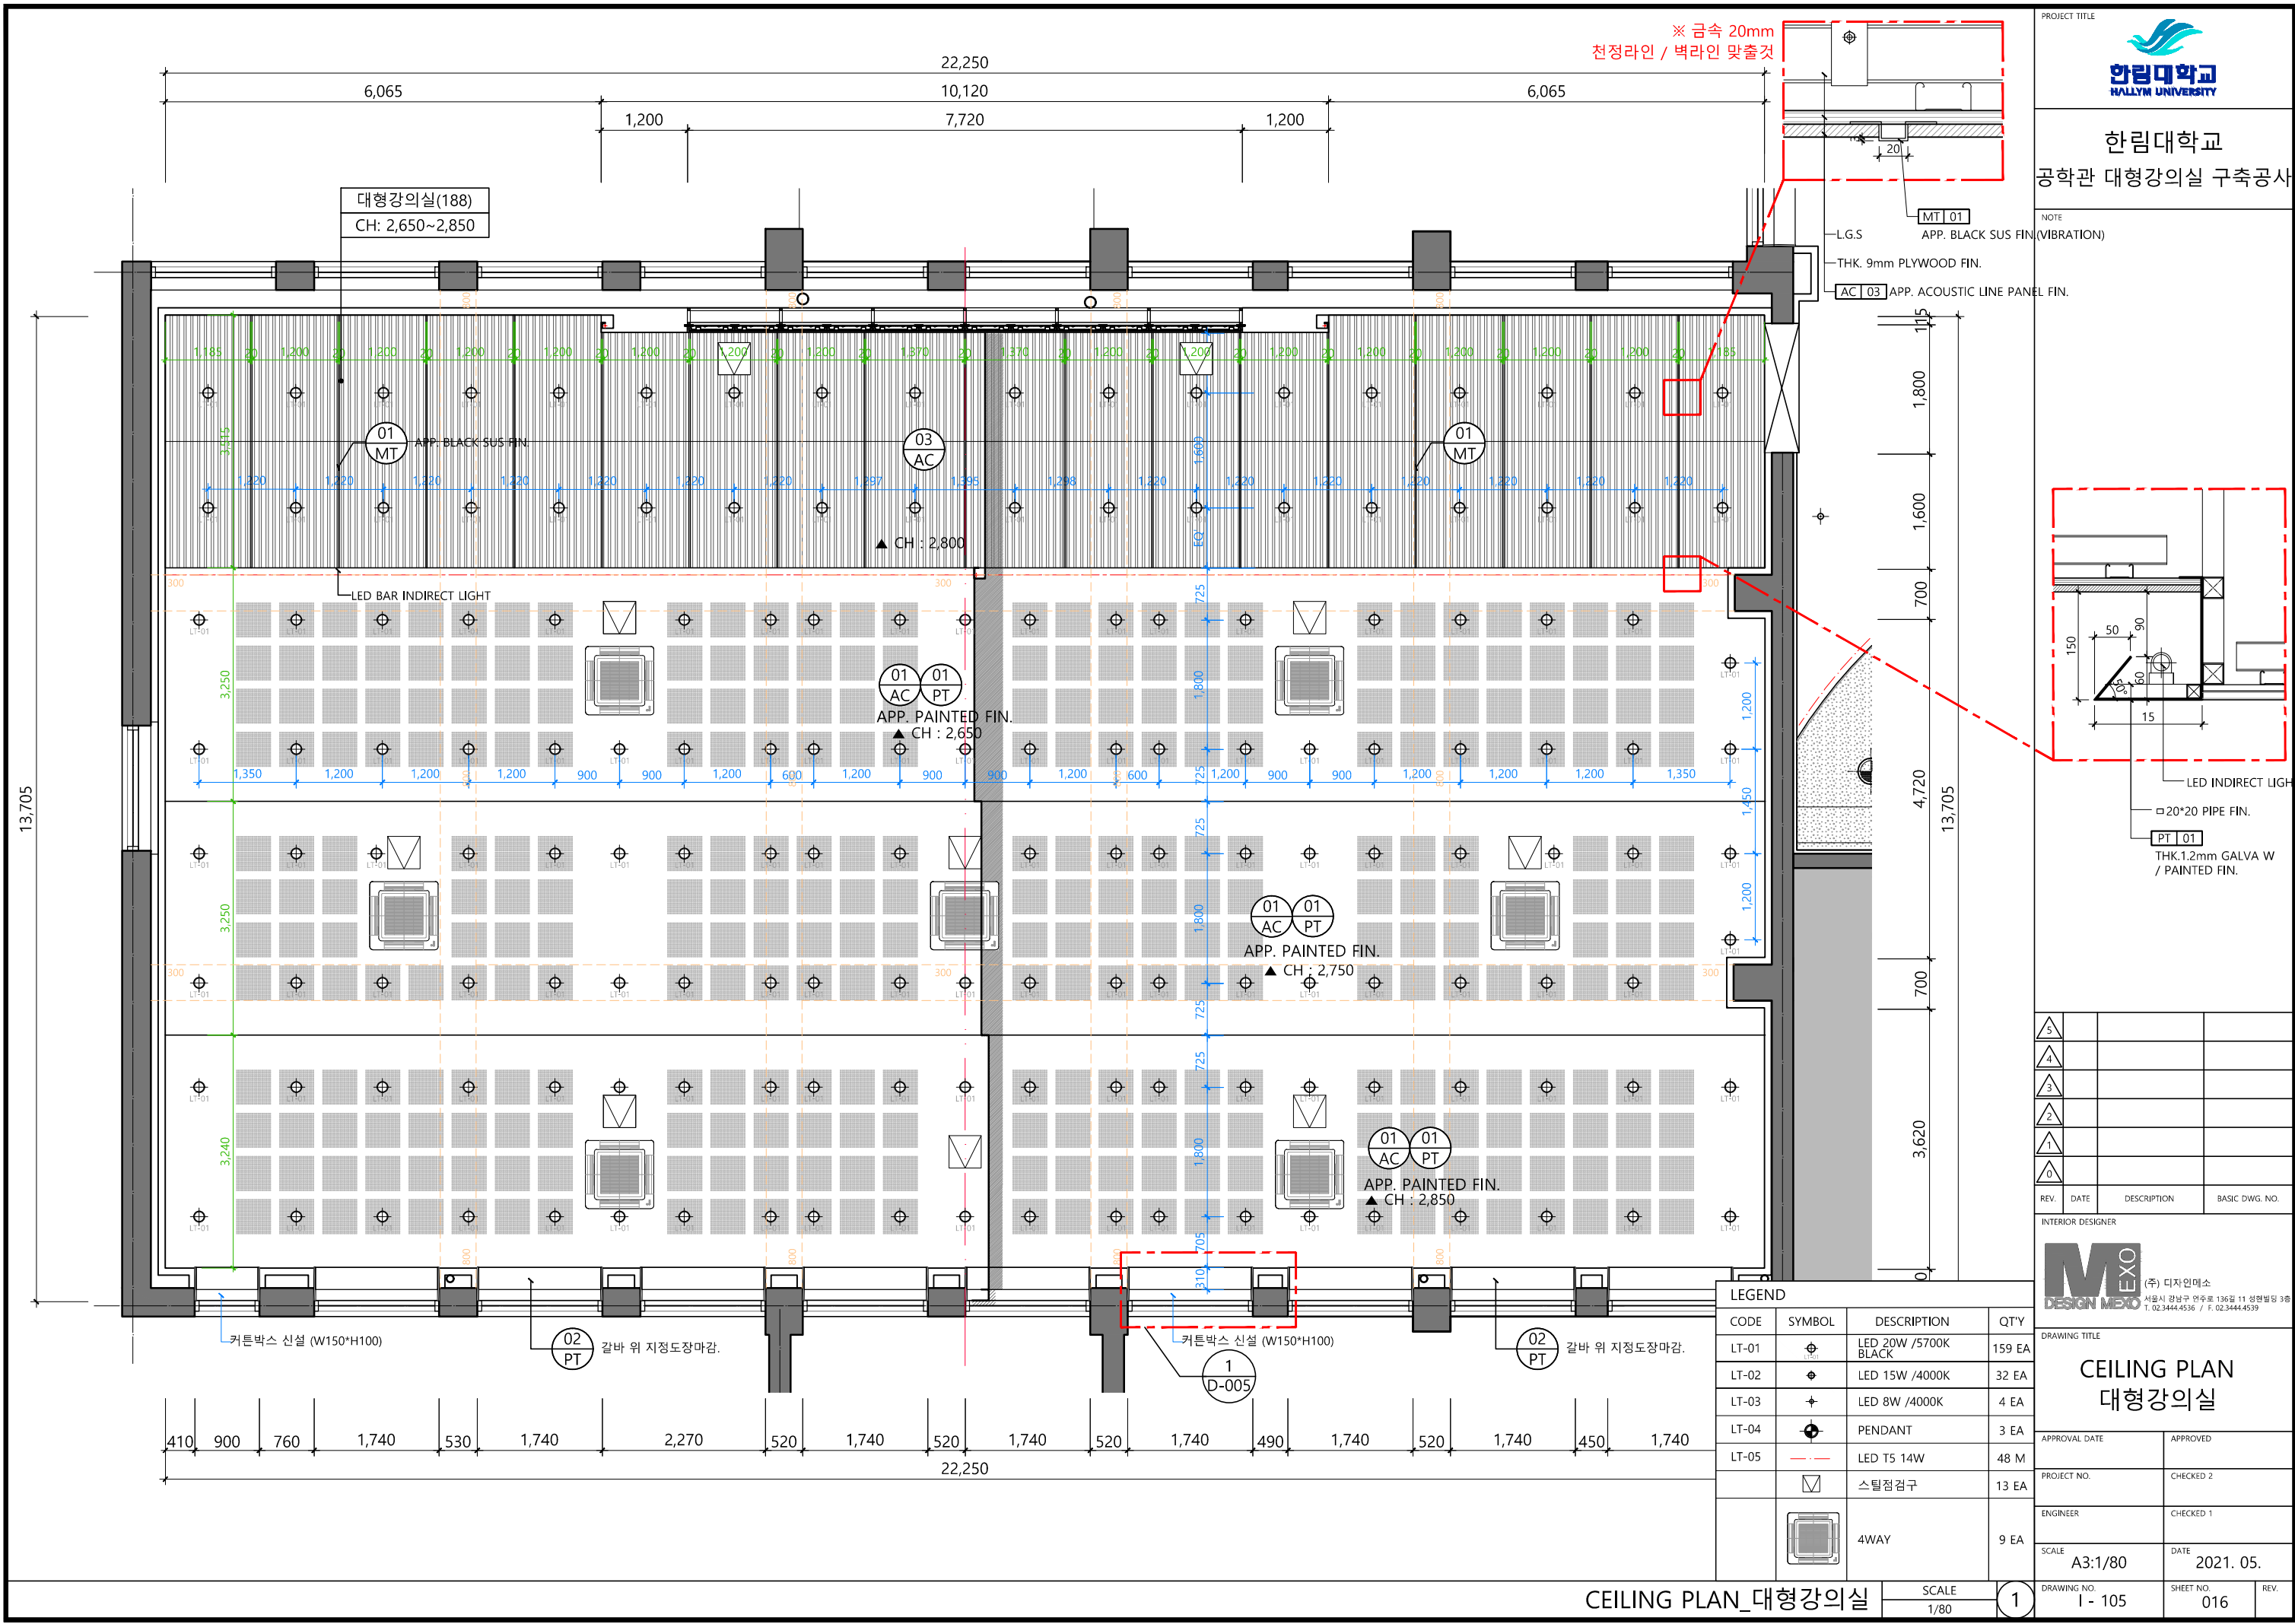




한림대학교
HALLYM UNIVERSITY

한림대학교
공학관 대형강의실 구축공사

NOTE
(VIBRATION)

MT | 01 APP. BLACK SUS FIN.
THK. 9mm PLYWOOD FIN.
AC | 03 APP. ACOUSTIC LINE PANEL FIN.

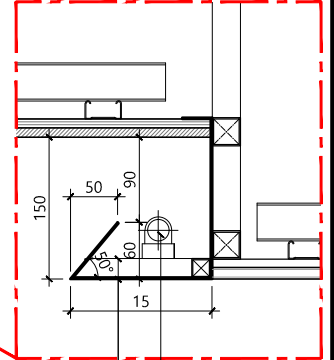

LED INDIRECT LIGHT
□ 20*20 PIPE FIN.
PT | 01 THK. 1.2mm GALVA W / PAINTED FIN.

5			
4			
3			
2			
1			
0			
REV.	DATE	DESCRIPTION	BASIC DWG. NO.



(주) 디자인메소
서울시 강남구 연수로 136길 11 천변빌딩 3층
T. 02.3444.4536 / F. 02.3444.4539

DRAWING TITLE

CEILING PLAN
대형강의실

APPROVAL DATE	APPROVED
PROJECT NO.	CHECKED 2
ENGINEER	CHECKED 1
SCALE A3:1/80	DATE 2021. 05.
DRAWING NO. I - 105	SHEET NO. 016
	REV.

